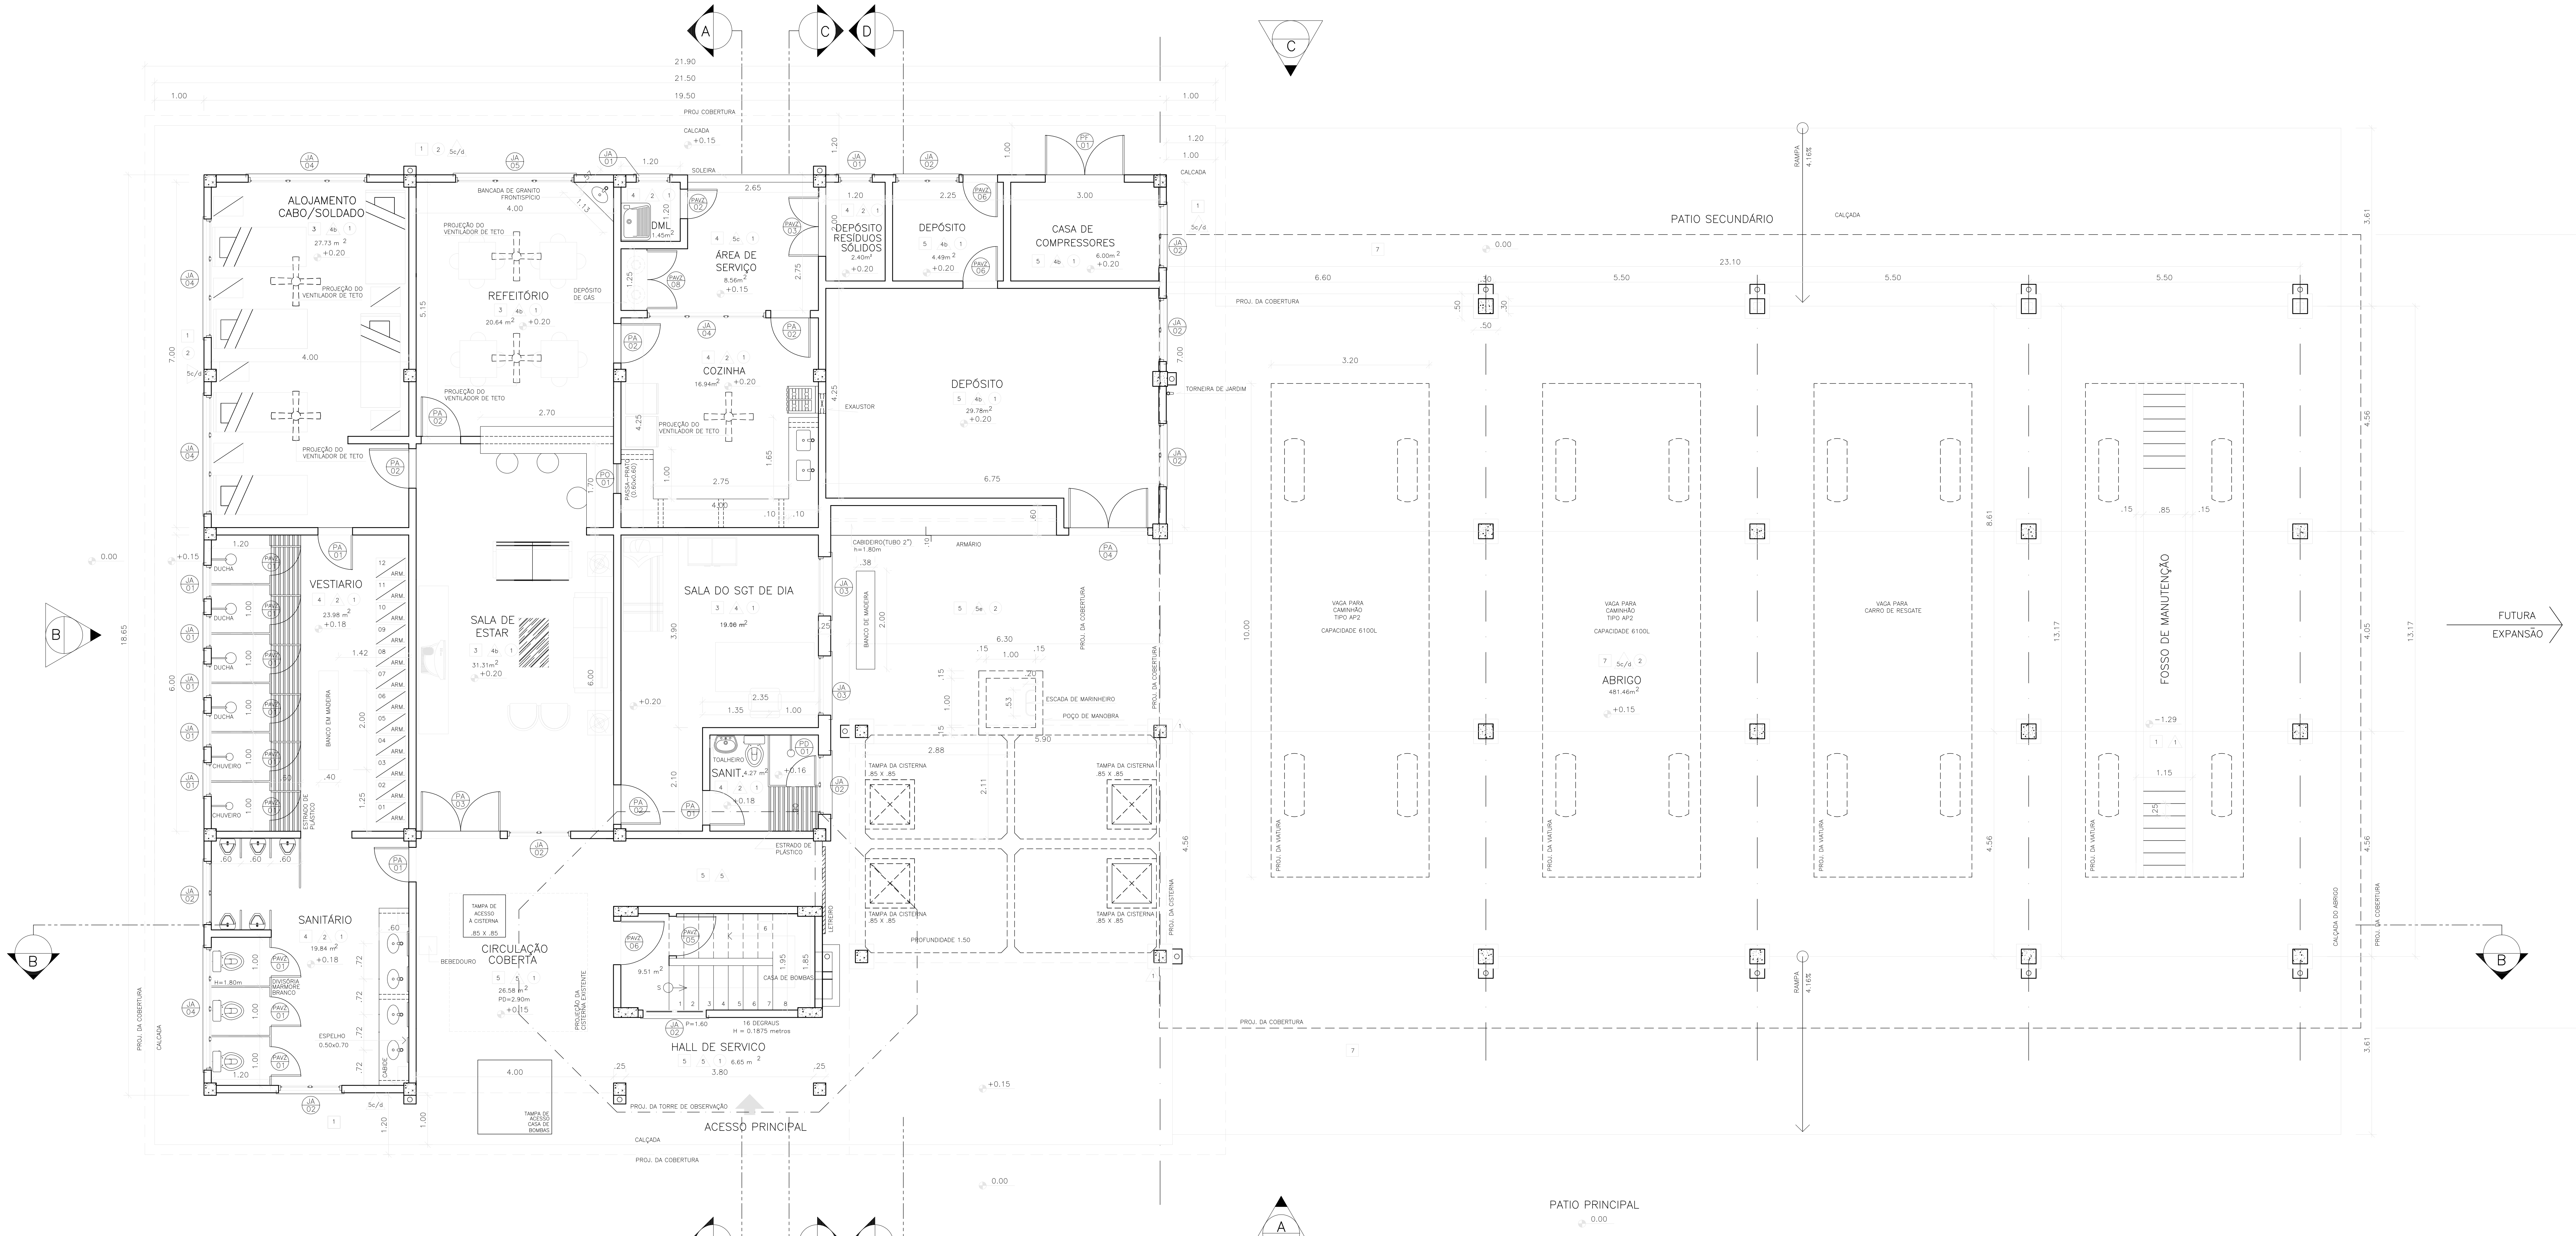
ALOJAMENTO CABO/SOLDADO
REFEITÓRIO
DML
ÁREA DE SERVIÇO
DEPÓSITO RESÍDUOS SÓLIDOS
DEPÓSITO
CASA DE COMPRESSORES
COZINHA
DEPÓSITO
VESTIÁRIO
SALA DE ESTAR
SALA DO SGT DE DIA
SANIT.
SANITÁRIO
CIRCULAÇÃO COBERTA
HALL DE SERVIÇO
ACESSO PRINCIPAL
PATIO SECUNDÁRIO
PATIO PRINCIPAL
ABRIGO
VAGA PARA CAMINHÃO TIPO AP-2 CAPACIDADE 6100L
VAGA PARA CARRO DE RESGATE
FOSSO DE MANUTENÇÃO
FUTURA EXPANSÃO
RAMPA
PROJ. DA COBERTURA
CALÇADA
TAMPA DA CISTERNA
POÇO DE MANOBRA
ESCADA DE MARINHEIRO
BANCO EM MADEIRA
TORNEIRA DE JARDIM
A
B
C
D

PLANTA BAIXA
ESC–1/50 UNID–m


SALA DE OBSERVAÇÃO
DIVISÓRIA PAINEL/VIDRO/VIDRO PEITORIL = 0.80
ESCADA DE MARINHEIRO
SHAFT PARA HIDRÁULICA
SHAFT PARA ELÉTRICA
A
B
C
D

PLANTA BAIXA DA SALA DE OBSERVAÇÃO
ESC–1/50 UNID–m

QUADRO DE ESPECIFICAÇÕES:

PISOS

Nº	PAVIMENTAÇÃO	RODAPÉ
1	CIMENTADO C/ JUNTA SECA 80X80cm	ARGAMASSA C/ 25cm
2	ARGAMASSA ARMADA C/ JUNTA DE 80X80cm	ARGAMASSA C/ 25cm
3	CERÂMICA PEI–4 45X45cm	CERÂMICA 8,5X45cm
4	CERÂMICA ANTIDERRAPANTE PEI–5	——
5	ARGAMASSA ARMADA POLIDA	ARGAMASSA ARMADA COM 10cm
6	ARGAMASSA ARMADA SEMI–POLIDA	ARGAMASSA ARMADA COM 10cm
7	CONFORME PROJETO DE INFRAESTRUTURA	——

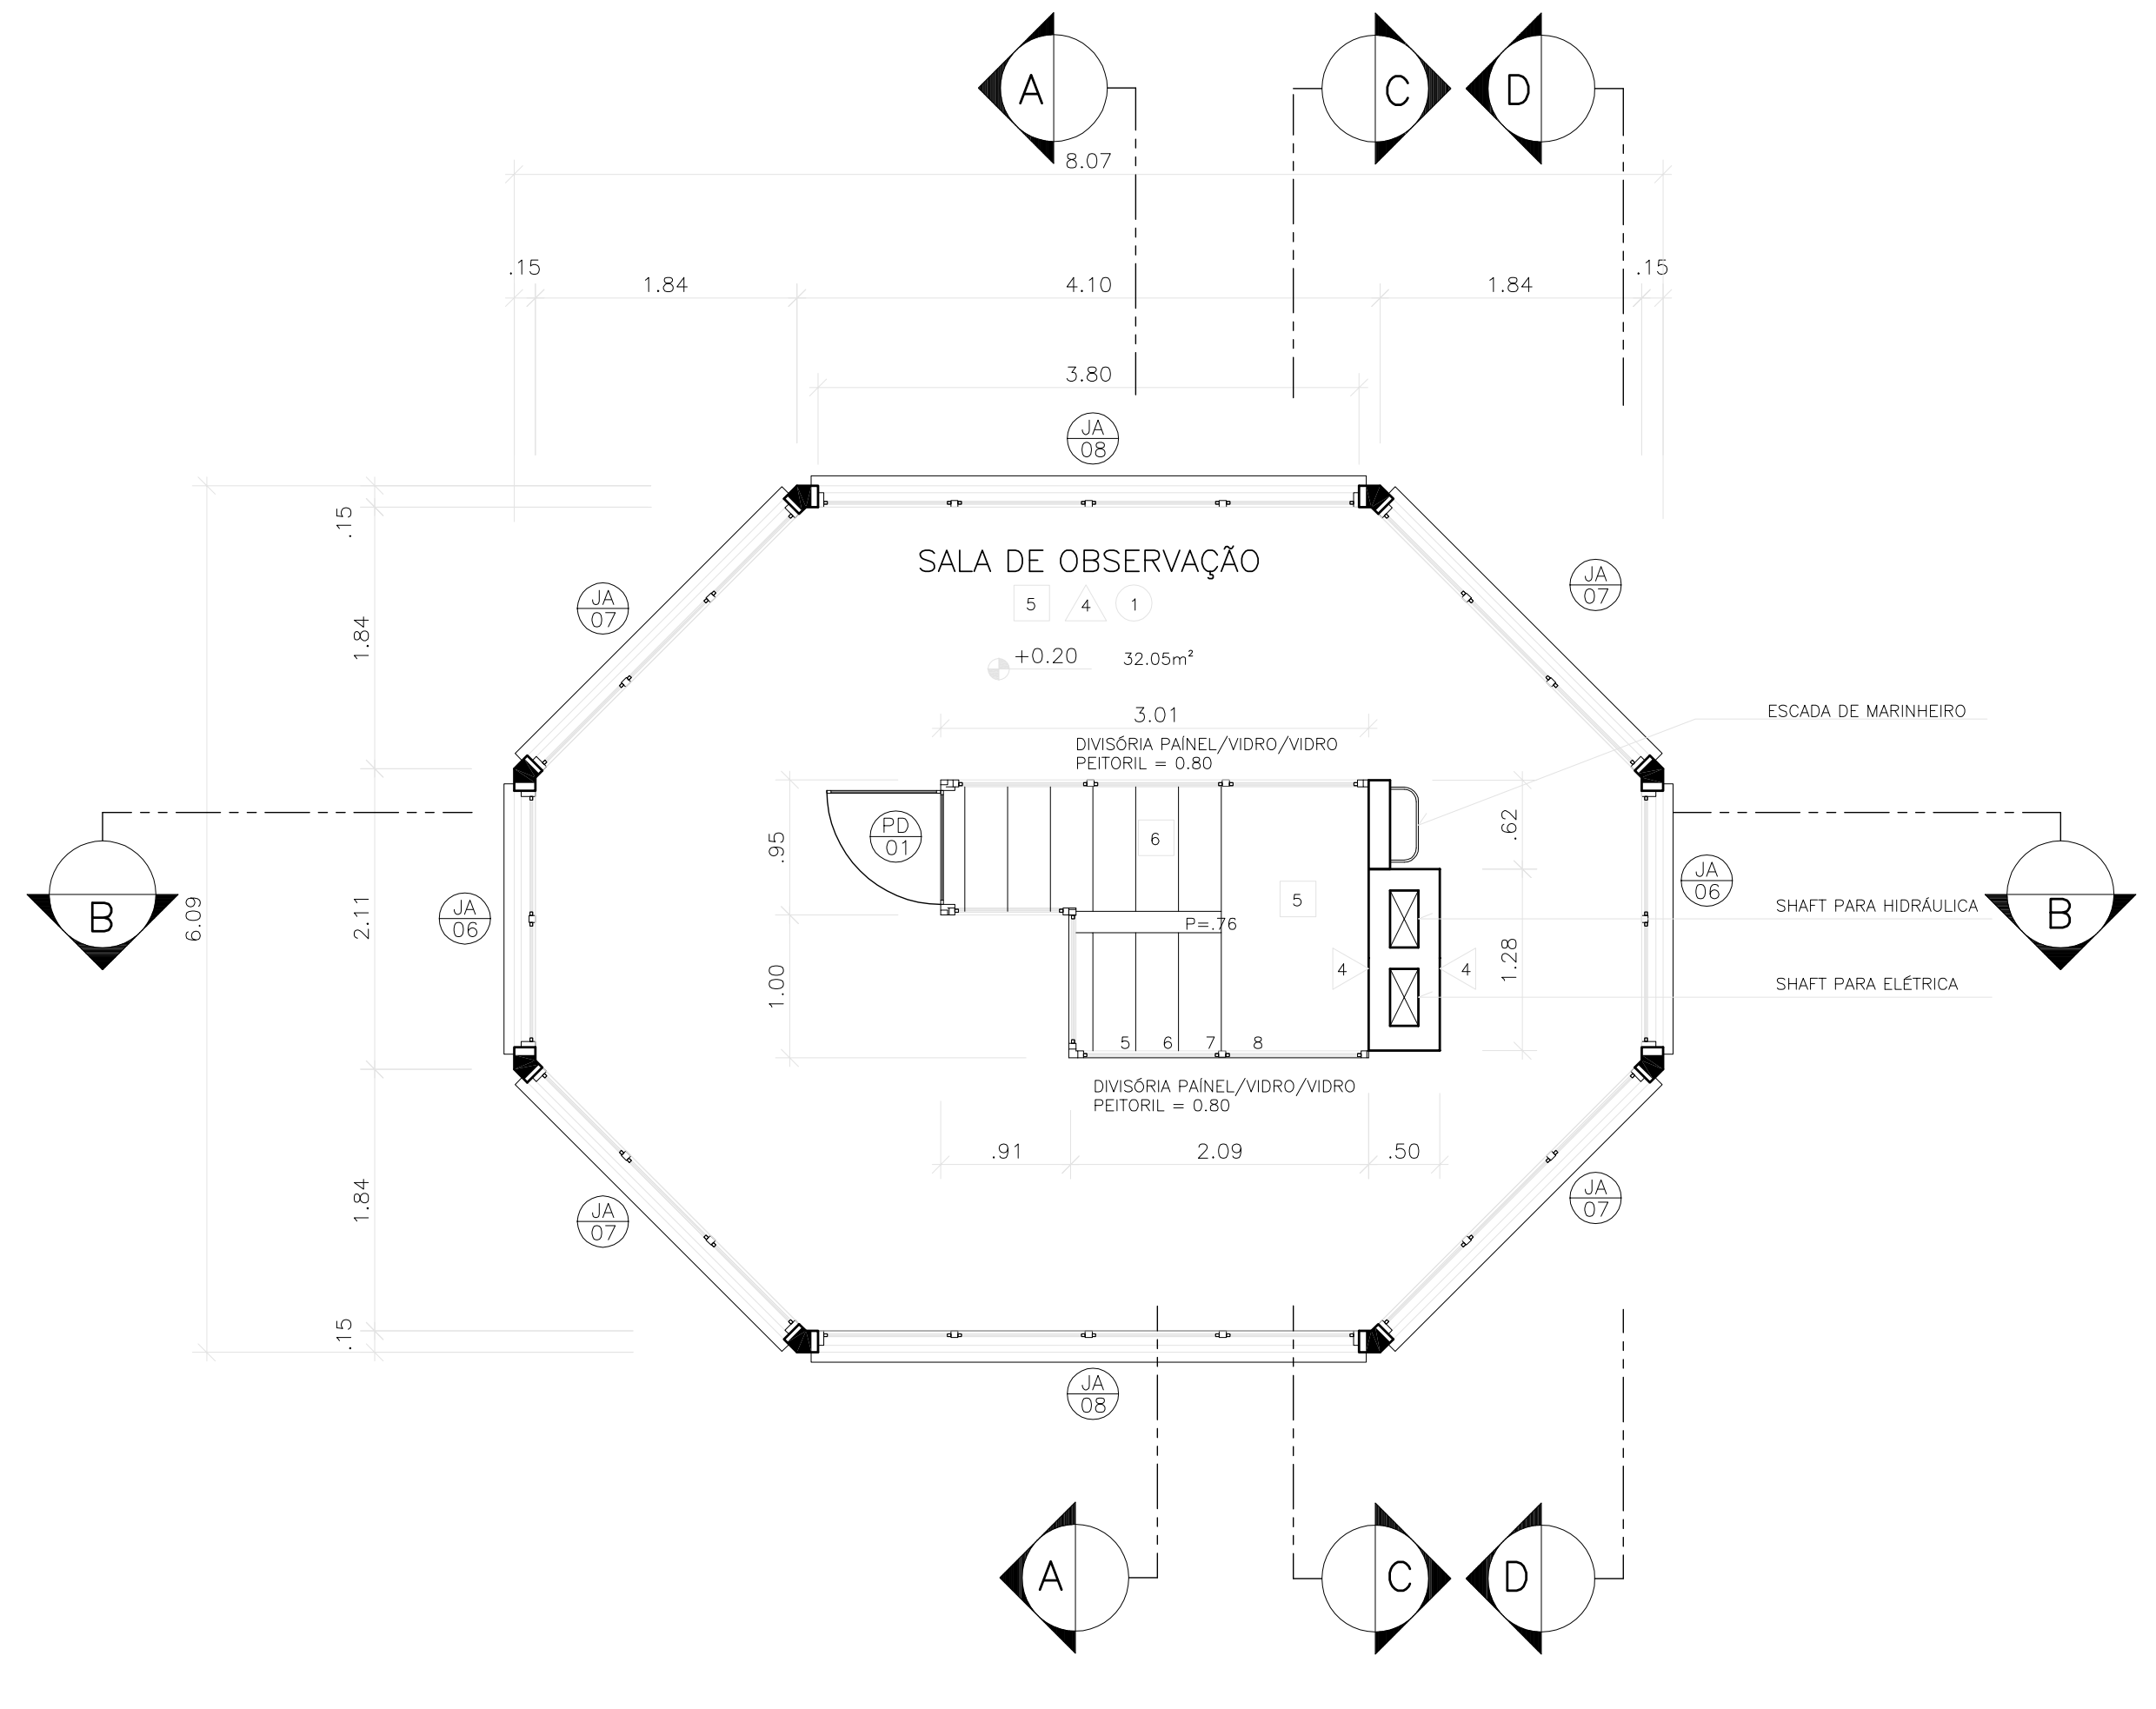PAREDES

Nº	REVESTIMENTO	PINTURA
1	CHAPISCO, EMBOÇO c:a:s(t–1:2:3)	TINTA ACRÍLICA (ver item 04.01.569 da Especificação
2	CERÂMICA 20X30cm	——
3	PAINEL ABSORVENTE DE ESPUMA FLEXÍVEL	——
4	CHAPISCO; MASSA ÚNICA	TINTA ACRÍLICA (ver item 04.01.569 da Especificação
5	CHAPISCO; MASSA ÚNICA IMPERMEABILIZADA	TINTA ACRÍLICA (ver item 04.01.569 da Especificação

TETOS

Nº	REVESTIMENTO	PINTURA
1	CHAPISCO; MASSA ÚNICA	TINTA PVA BRANCA
2	TELHA APARENTE	TINTA ACRÍLICA BRANCA

ESQUADRIAS

Nº	DIMENSOES (m)	Q	DET
PA01	.70 X 2.10	3	
PA02	.80 X 2.10+.60	5	
PA03	1.60 X 2.10 +.60	1	
PA04	1.60 X 2.20	2	
PAVZ01	.55 X 1.80	10	
PAVZ02	.60 X 2.10	1	
PAVZ03	1.20 X 2.10	1	
PAVZ04	.80 X .85	1	
PAVZ05	.70 X 2.10	1	
PAVZ06	.80 X 2.10	3	
PAVZ07	.80 X 1.20	10	
PAVZ08	1.20 X 1.00	1	
PD01	.80 X 2.20	1	
PO01	.60 X .60	1	
PF01	1.60 X 2.50	1	

ESQUADRIAS

Nº	DIMENSOES (cm)	Q	DET
JA01	0.60 X 0.60	7	
JA02	1.20 X 0.60	9	
JA03	1.20 X 1.10 + 0.60	2	
JA04	2.40 X 0.60	5	
JA05	2.40 X 1.20	1	
JA06	1.80 X 2.00	2	P=.80
JA07	2.50 X 2.00	4	P=.80
JA08	3.80 X 2.00	2	P=.80

ÁREA CONSTRUÍDA 1º PAV. ABRIGO	317.61 m²
ÁREA CONSTRUÍDA 1º PAV. EDIFICAÇÃO PRINCIPAL	312.42 m²
ÁREA CONSTRUÍDA 2º PAV. + RESERVAT. ELEVADO	71.52 m²
ÁREA TOTAL	701.55 m²
ÁREA COBERTA	830.57 m²

COMANDO DA AERONAUTICA
Diretoria de Engenharia da Aerọnautica
SUBDIRETORIA DE ESTUDOS E PROJETOS
APROVO
Brig Eng LUIZ SÉRGIO HEINZELMANN
SUBDIRETOR DE ESTUDOS E PROJETOS
CREA: 53.302–D/RJ
DE ACORDO COM PORTARIA .../SDE, DE
DE ..... DE .... DE 2011.

COMAER
DIRETORIA DE ENGENHARIA DA AERONÁUTICA
SUBDIRETORIA DE ESTUDOS E PROJETOS
EP–21

AEROPORTO DE SÃO GABRIEL DA CACHOEIRA (UAUPÉS/SBUA)
SEÇÃO DE CONTRAINCÊNDIO – CATEGORIA 6
PROJETO DE REFORMA E AMPLIAÇÃO – ARQUITETURA
PLANTAS BAIXAS DE EXECUÇÃO (PAV. TÉRREO E SALA DE OBSERVAÇÃO)

UNIDADE	DATA	ESCALA
m	ABR/11	1/50

Nº DO ARQUIVO TÉCNICO
AM008.24–01.A001

	RUBRICA	
VISTO : Cel Eng ROBSON		IDENT 277441 – COMAER
CONFERIDO :		CREA
PROJETISTA : ARQ. PAOLETTA		CREA 81.1.0353–2D/RJ
DESENHISTA :		

Nº DO ARQUIVO ELETRÔNICO

MODIFICAÇÕES	DATA	RESPONSÁVEL

SUBSTITUI A:/SUBSTITUIDO POR:

AM008.24-01.A001

CORES	Esp. mm
Cor 30	0.100
Blue	0.190
Cor 09	0.190
Cor 10	0.275
Yellow	0.275
Red	0.350
Cyan	0.430
Magenta	0.550
Green	0.770
plotagem na escala 10:1	

FORMATO A0L al 840x1373